Floor 0

To another room
Balcony
Next floor
Window
Door
Border between two rooms (without doors)
W1_50 Name of a wall
6 Name of a room

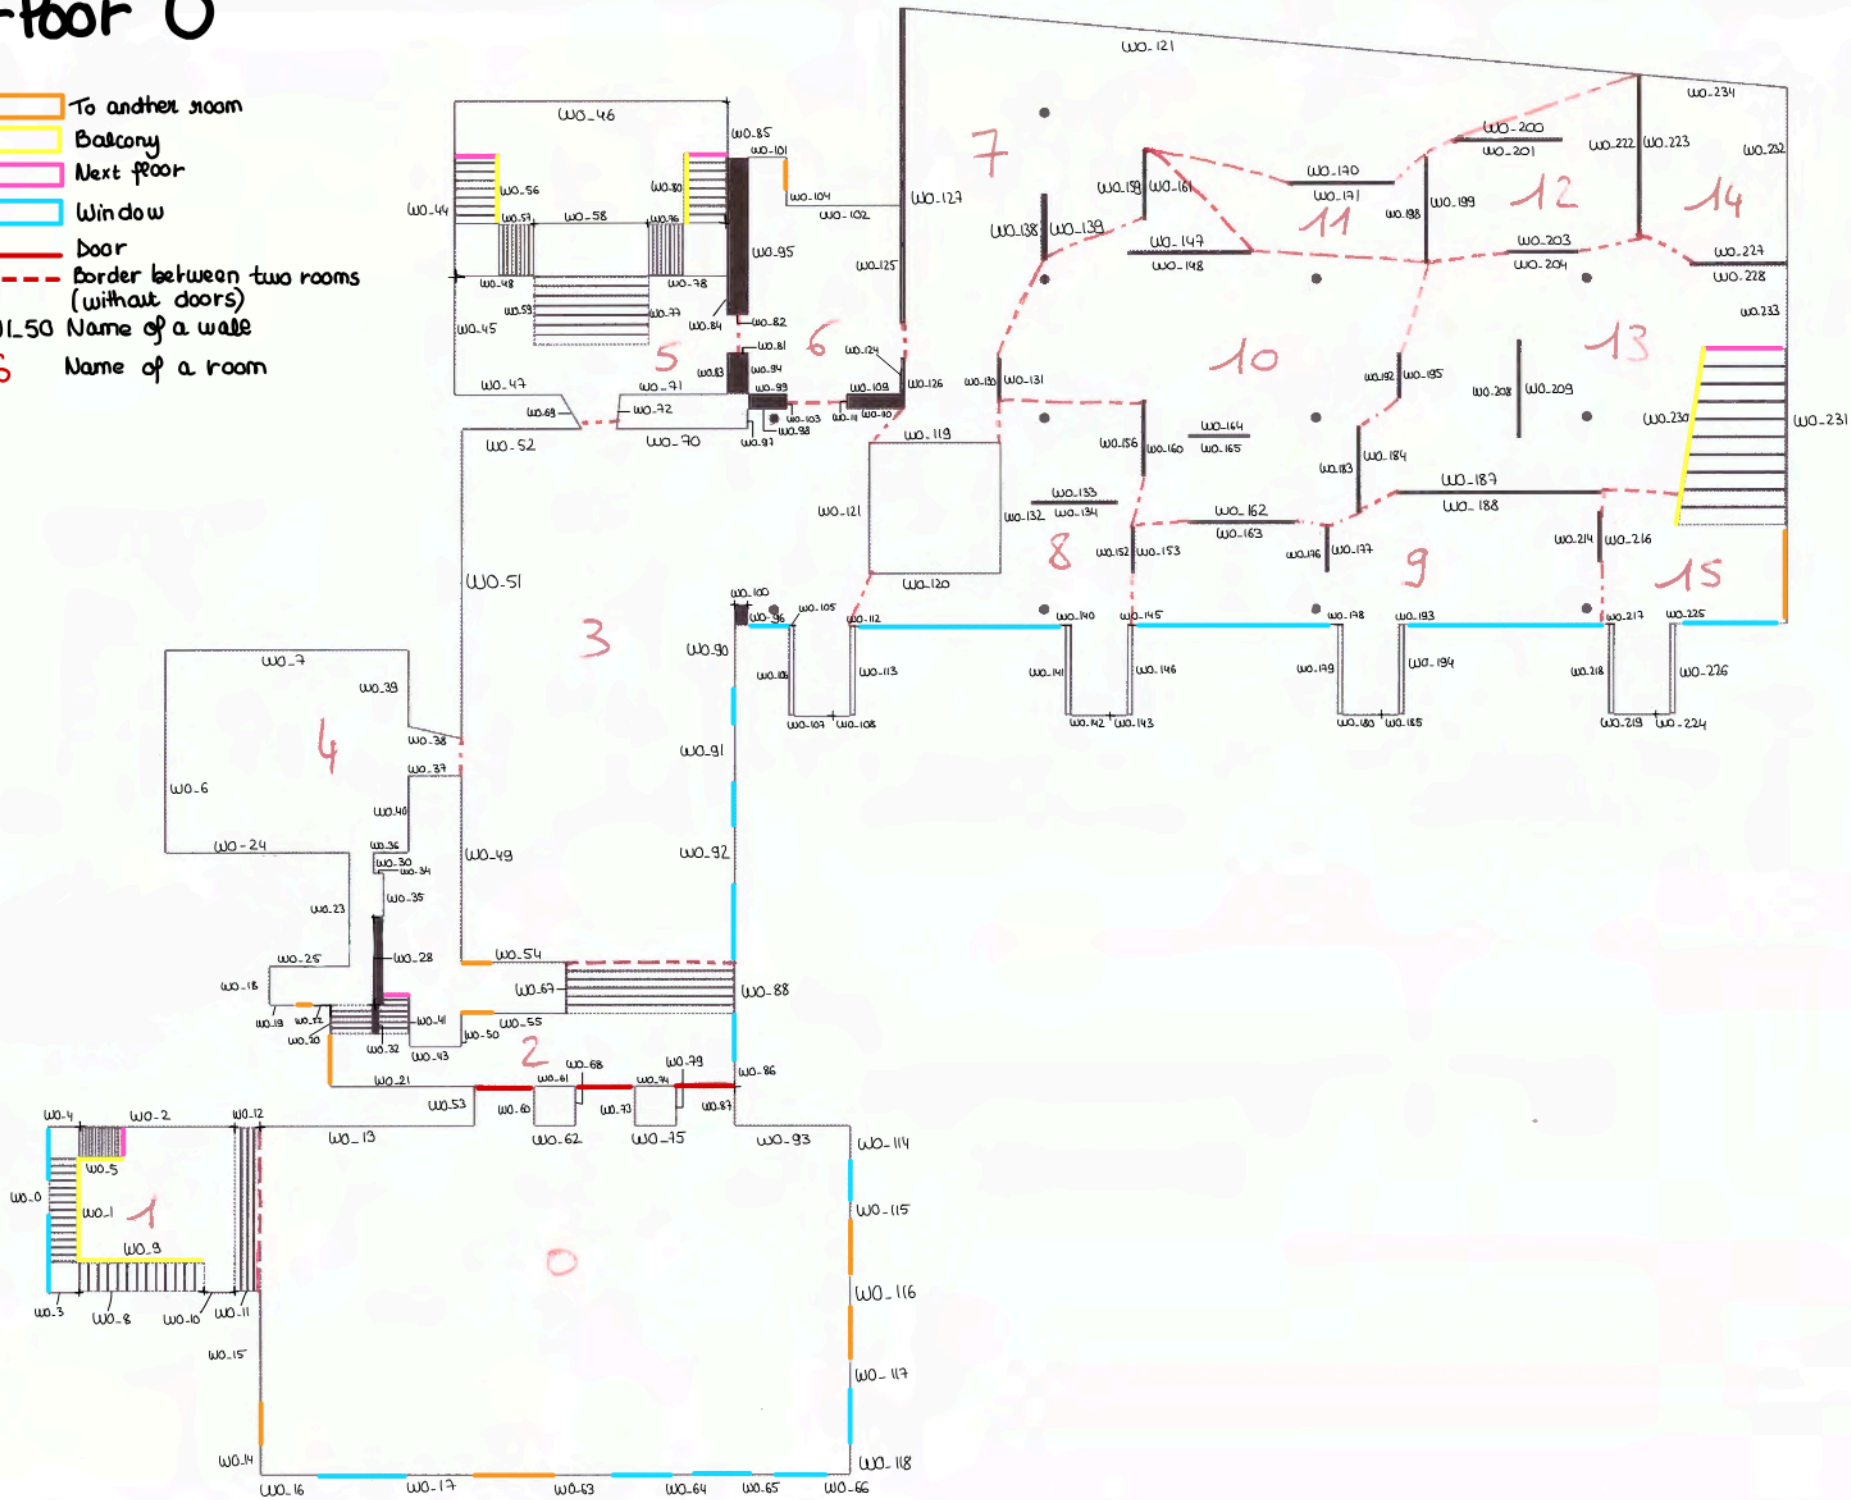

Floor 1

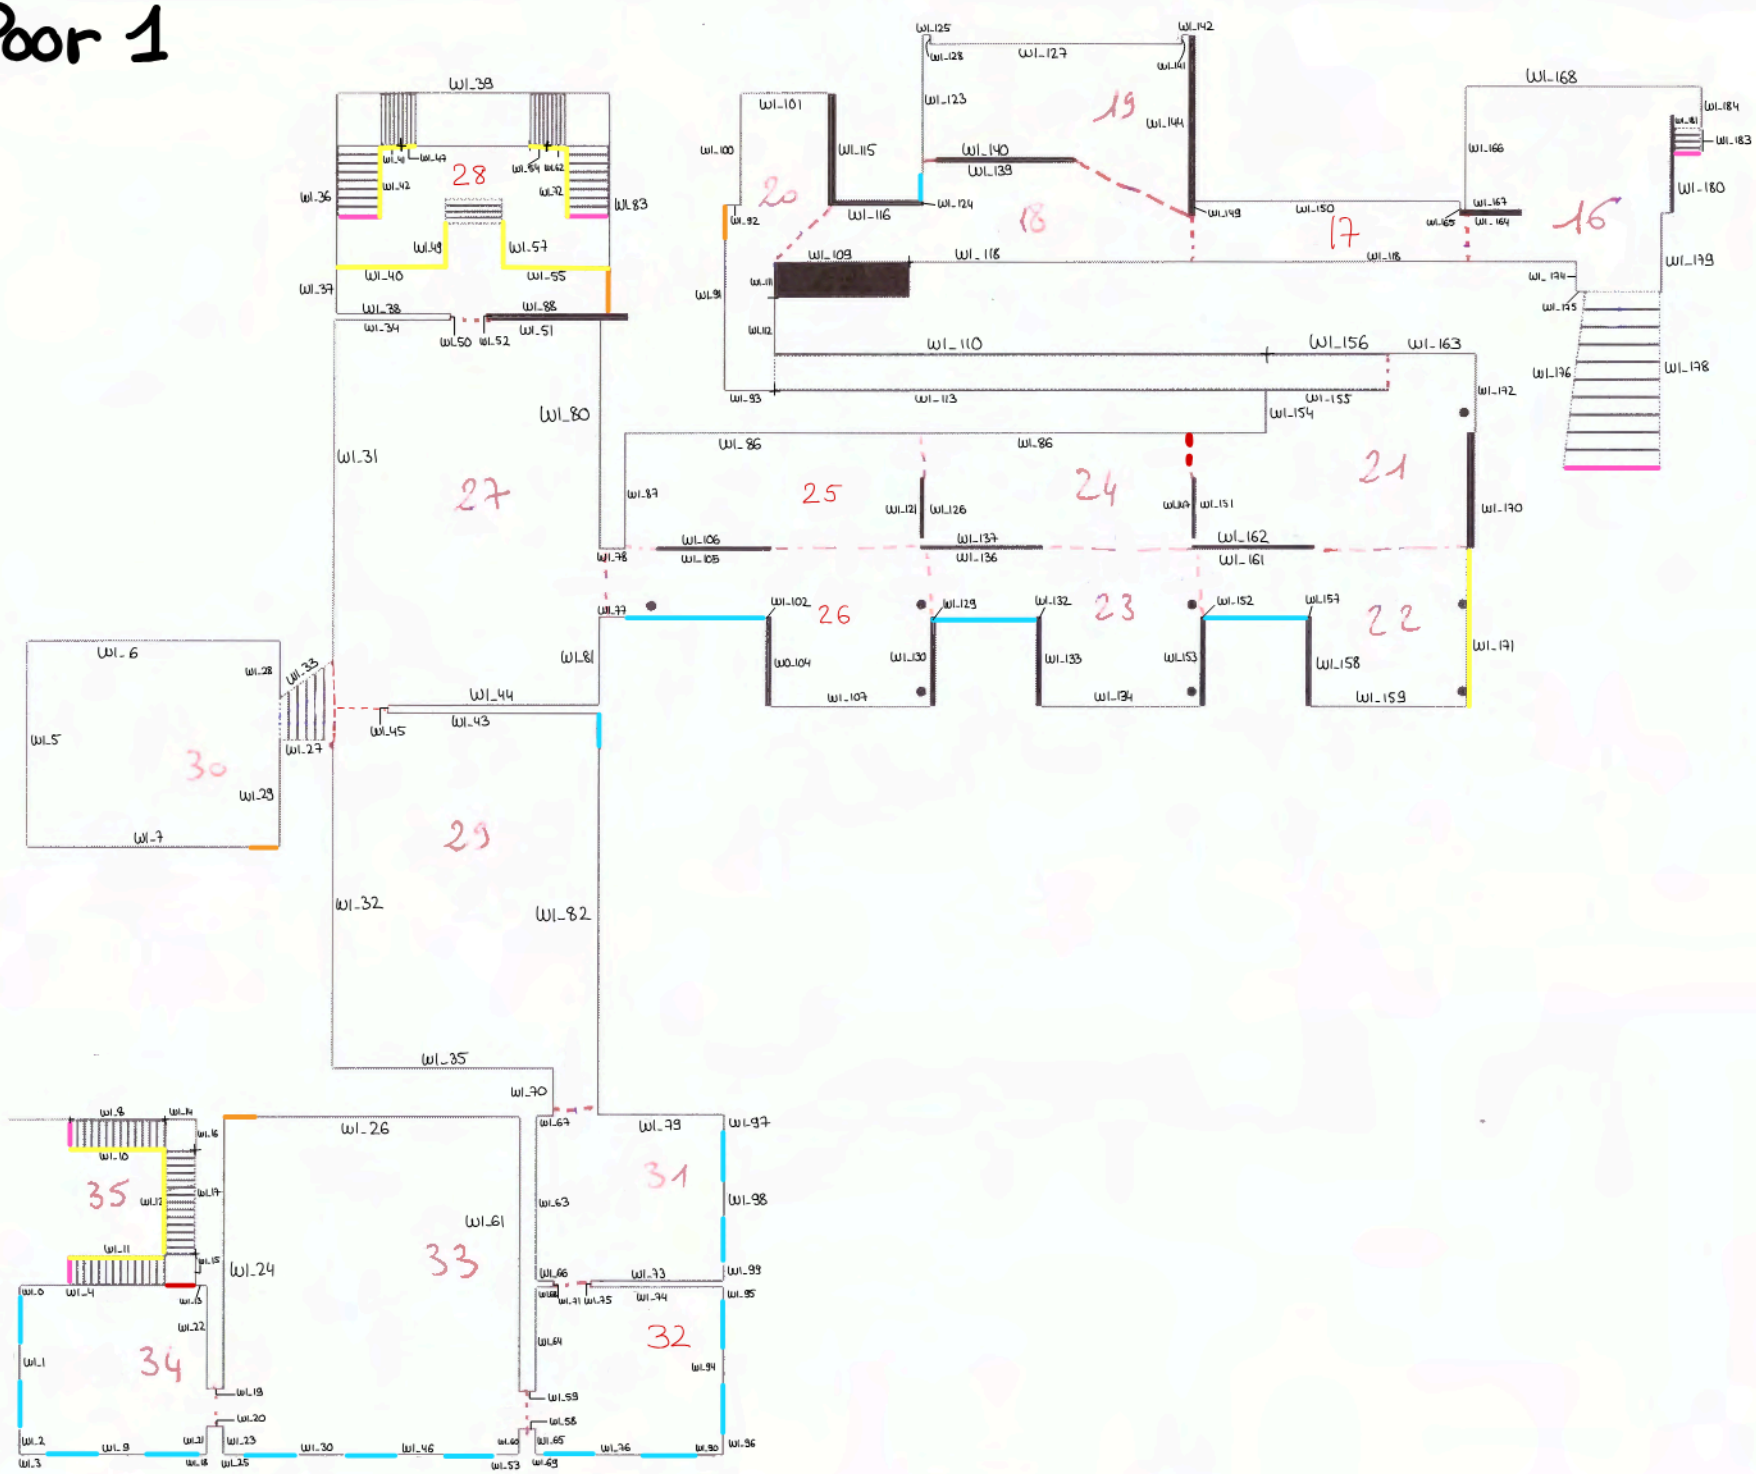

FPoor 2

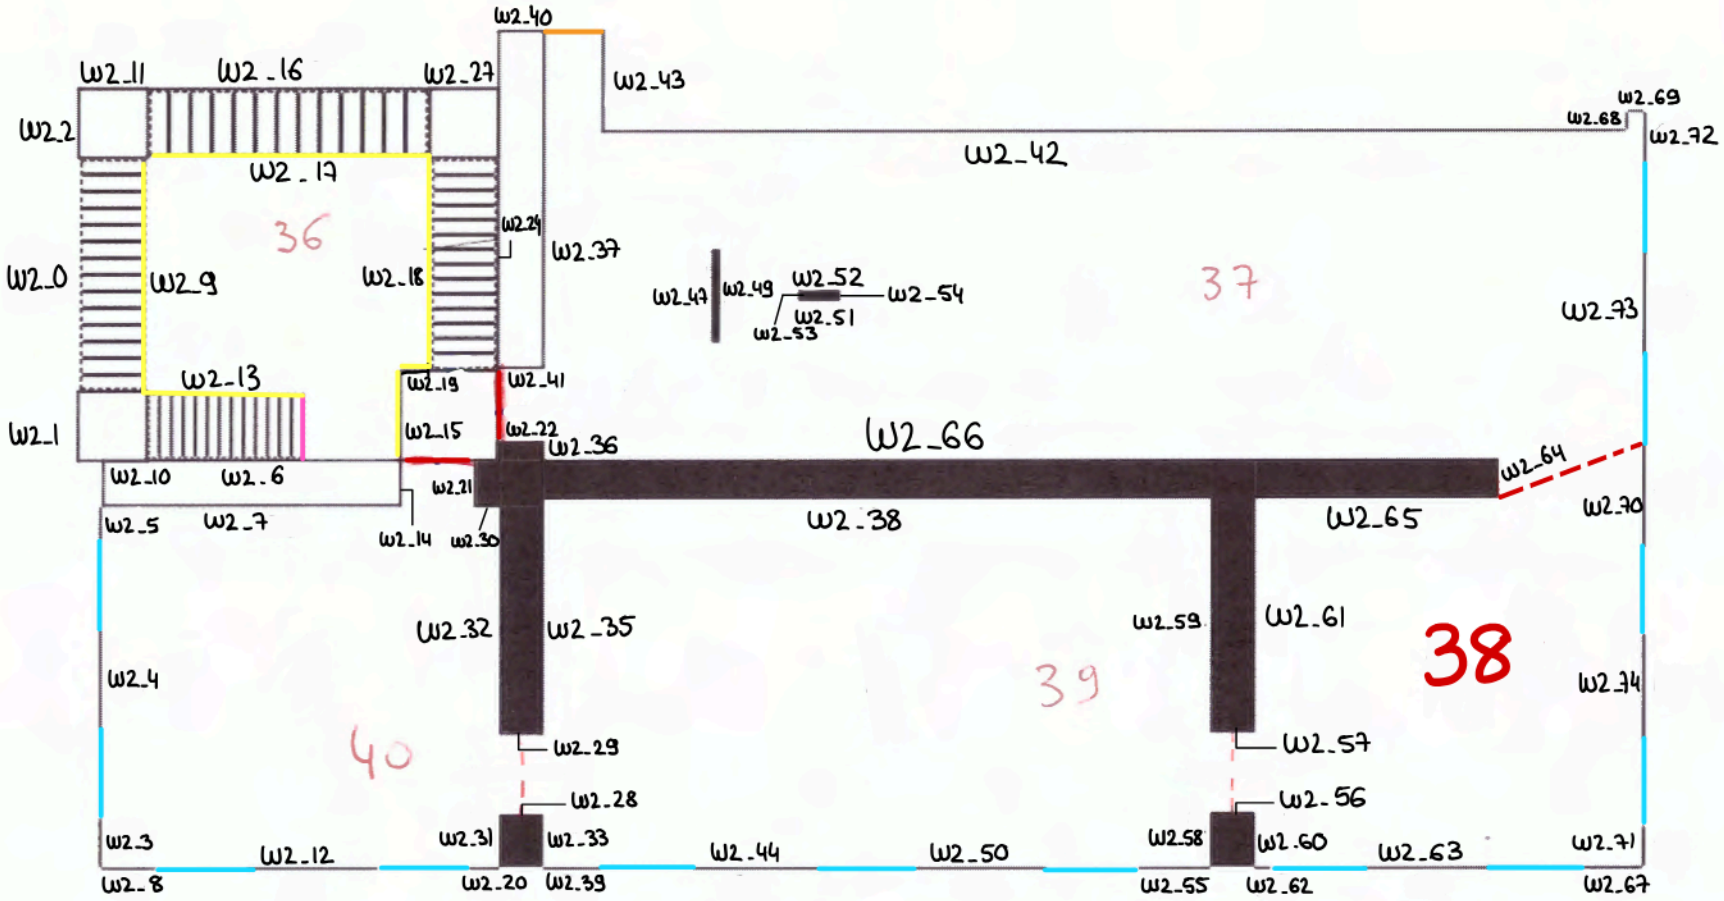
W2_40
W2_11
W2_16
W2_27
W2_43
W2_69
W2_68
W2_72
W2_2
W2_42
W2_17
36
W2_24
W2_37
W2_0
W2_9
W2_18
W2_47
W2_49
W2_52
W2_54
W2_51
W2_53
37
W2_73
W2_13
W2_19
W2_41
W2_1
W2_15
W2_22
W2_36
W2_66
W2_64
W2_10
W2_6
W2_21
W2_70
W2_5
W2_7
W2_14
W2_30
W2_38
W2_65
W2_32
W2_35
W2_59
W2_61
38
W2_4
39
W2_74
40
W2_29
W2_57
W2_28
W2_56
W2_3
W2_12
W2_31
W2_33
W2_44
W2_50
W2_58
W2_60
W2_63
W2_71
W2_8
W2_20
W2_39
W2_55
W2_62
W2_67